

СХЕМА РАСПОЛОЖЕНИЯ КИРПИЧНЫХ СТЕН НА ОТМ. 0,000


М 1:100

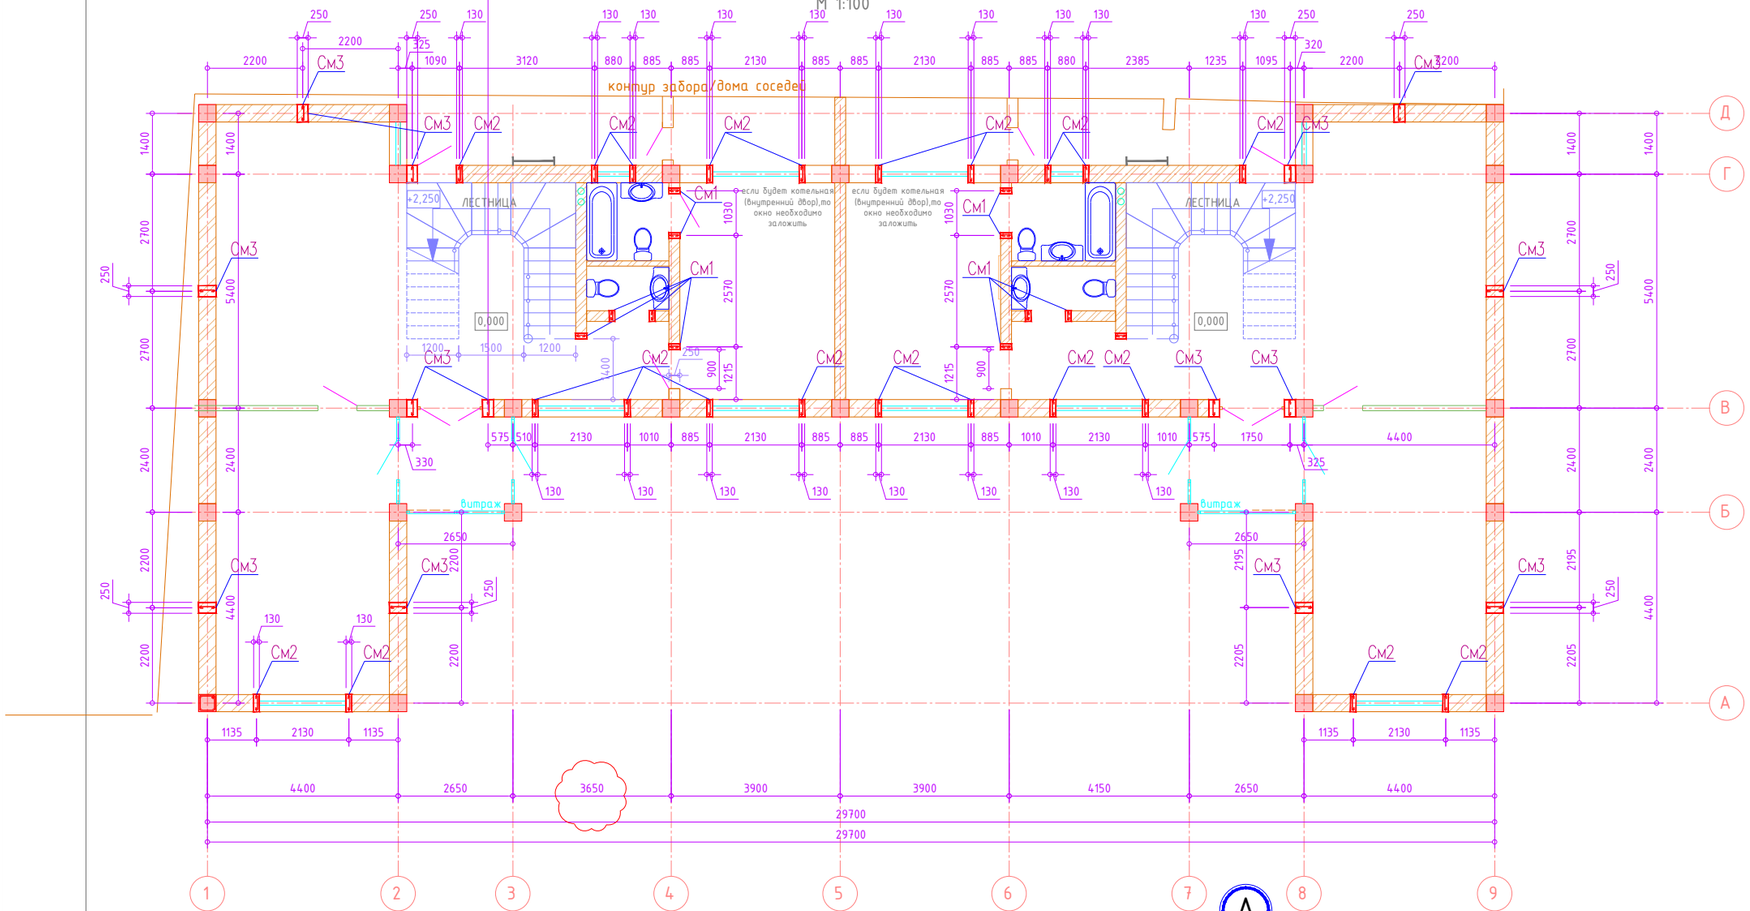


Перемычка Мп1
(армирование)

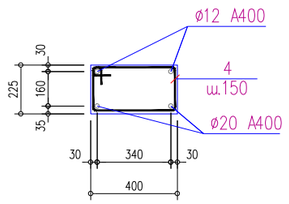


Перемычка Мп4
(армирование)

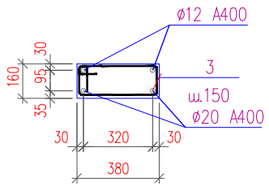


Перемычка Мп2
(армирование)

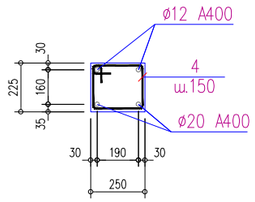


Перемычка Мп3
(армирование)

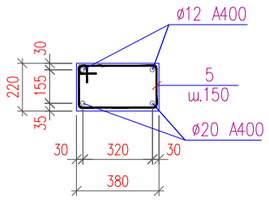


Сердечник См1
(армирование)
12 шт

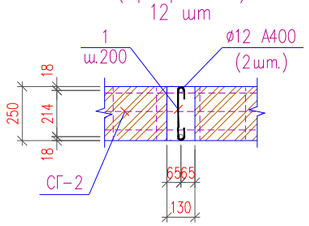


Сердечник См2
(армирование)
20 шт

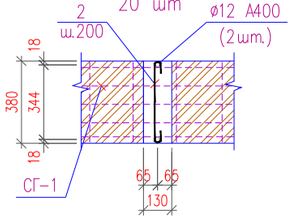

Сердечник См3
(армирование)
8 шт

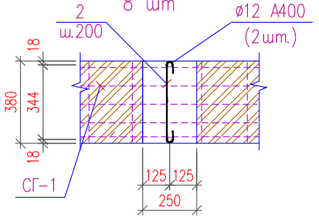

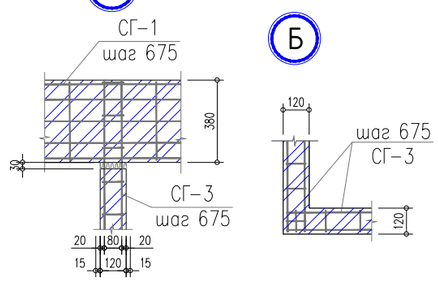

						Заказчик: Частное лицо	2022-КЖ
						«Строительство частного дома, расположенного по адресу: г. Ташкент»	
Изм.	Кол.уч.	Лист.	№док.	Подпись.	Дата.		
ГИП						Конструктивная часть Частный дом	Стадия: РП; Лист: 9.1; Листов: 50
Вед. инж.							
Исполн.						Схема расположения кирпичных стен на отм.0,00.	Ташкент 2022г.