

СХЕМА РАСПОЛОЖЕНИЯ КИРПИЧНЫХ СТЕН НА ОТМ. +3,300


М 1:100

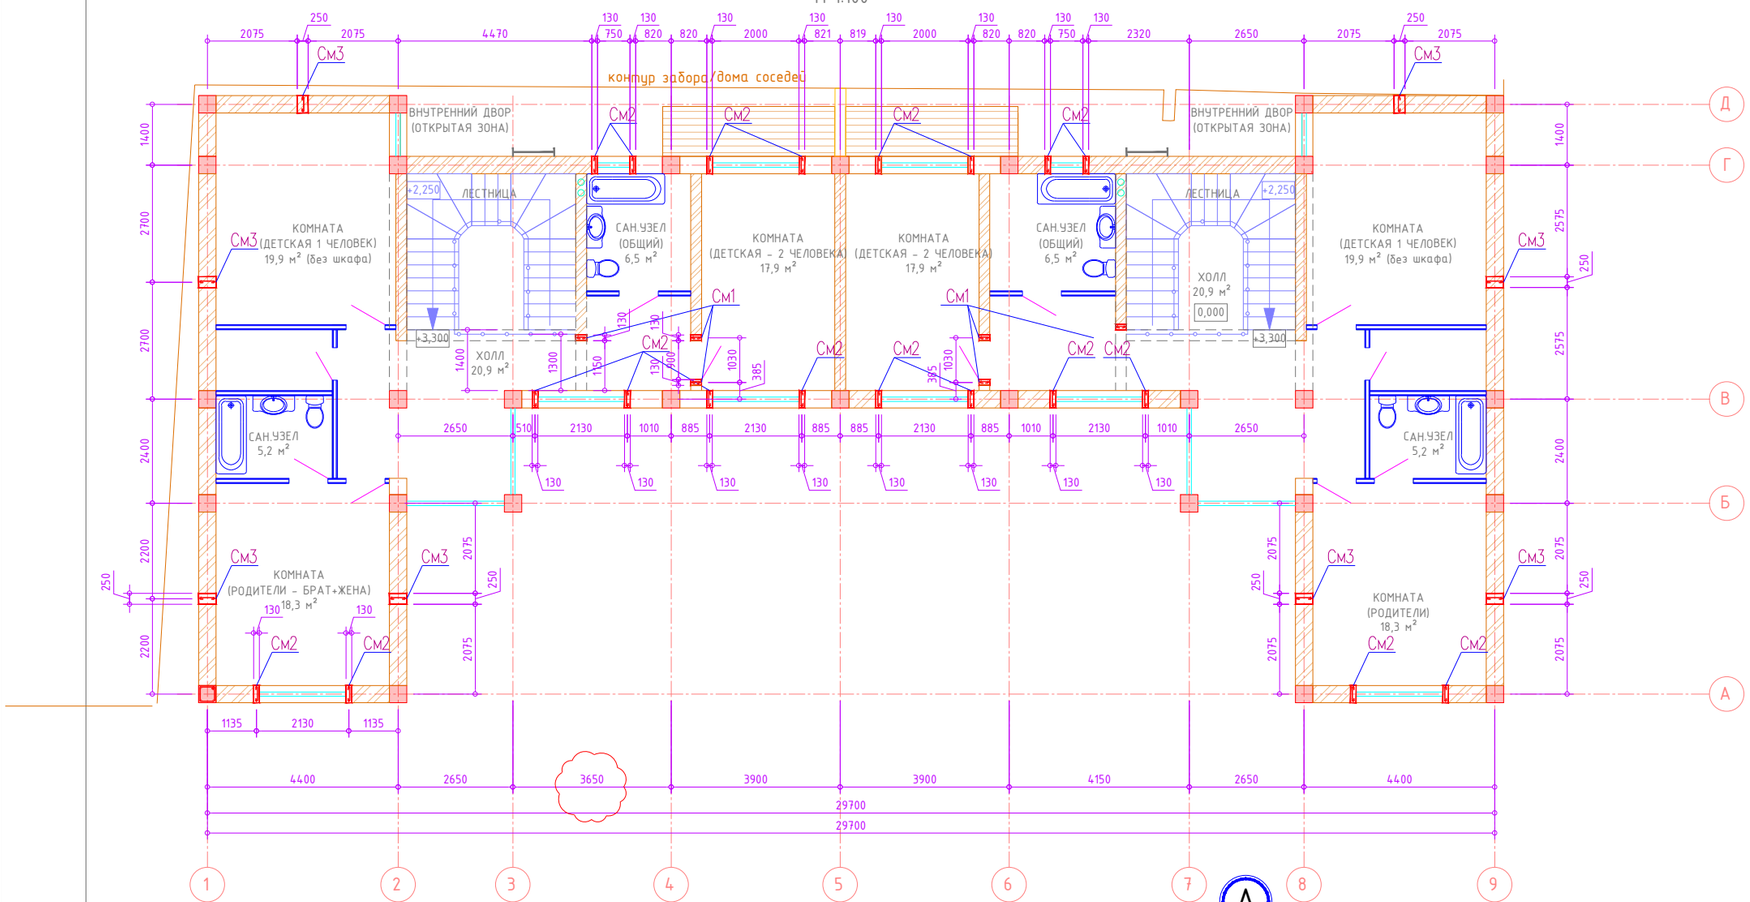


Сердечник См1
(армирование)
12 шт

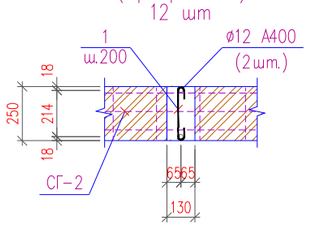


Сердечник См2
(армирование)
20 шт

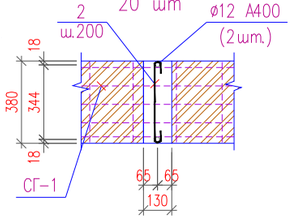


Сердечник См3
(армирование)
8 шт

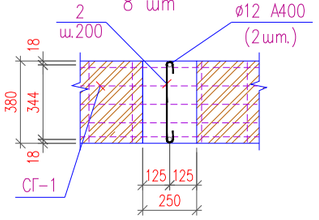


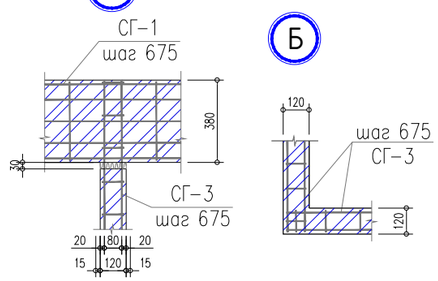


Перемычка Мп1
(армирование)

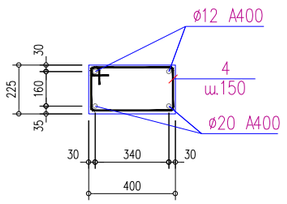


Перемычка Мп4
(армирование)

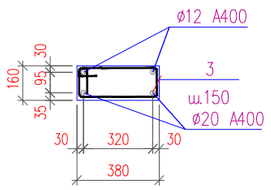

Перемычка Мп2
(армирование)

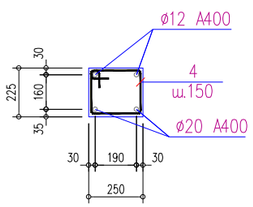

Перемычка Мп3
(армирование)

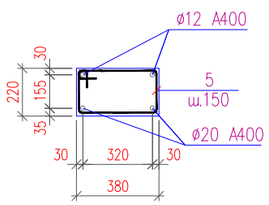

						Заказчик: Частное лицо	2022-КЖ
						«Строительство частного дома, расположенного по адресу: г. Ташкент»	
Изм.	Кол.уч.	Лист.	№док.	Подпись.	Дата.		
ГИП						Конструктивная часть Частный дом	Стадия: РП; Лист: 9.2; Листов: 50
Вед. инж.							
Исполн.						Схема расположения кирпичных стен на отм.+3.300	Ташкент 2022г.